

OBRA O SERVICIO

EDIFICIO "A":
SE INCLUYEN TRABAJOS DE:
-COLOCACION DE PANELES SOLARES




EDIFICIO "D":
SE INCLUYEN TRABAJOS DE:
-CONSTRUCCION DE EDIFICIO "D" QUE CONSISTE EN AULA DE MEDIOS EN ESTRUCTURA U-1C

OBRA EXTERIOR:
-CONSTRUCCION DE RED ELECTRICA PARA ALIMENTACION DE EDIFICIO "D"
-CONSTRUCCION DE CAPTADOR FLUVIAL

SUPERFICIES

TERRENO : 4,553 m2

NOTA:
LAS SUPERFICIES DE LOS TERRENOS HAN SIDO OBTENIDAS POR:
-CEDULA DE VALIDACION EN CAMPO.
-DOCUMENTACION QUE PROPORCIONAN LOS H. AYUNTAMIENTOS Y/O PLANTELES EDUCATIVOS, SIENDO ESTAS ESCRITURAS, ACTAS DE DONACION, LEVANTAMIENTOS O CROQUIS DEL PREDIO.
-ARCHIVO DIGITAL EXISTENTE EN LA BASE DE DATOS DE LA SUBDIRECCION DE PROYECTOS E INGENIERIA.
-CUALQUIER VARIACION EN LAS MEDIDAS DE LOS POLIGONOS SE REQUIERE REALIZAR LEVANTAMIENTO TOPOGRAFICO.

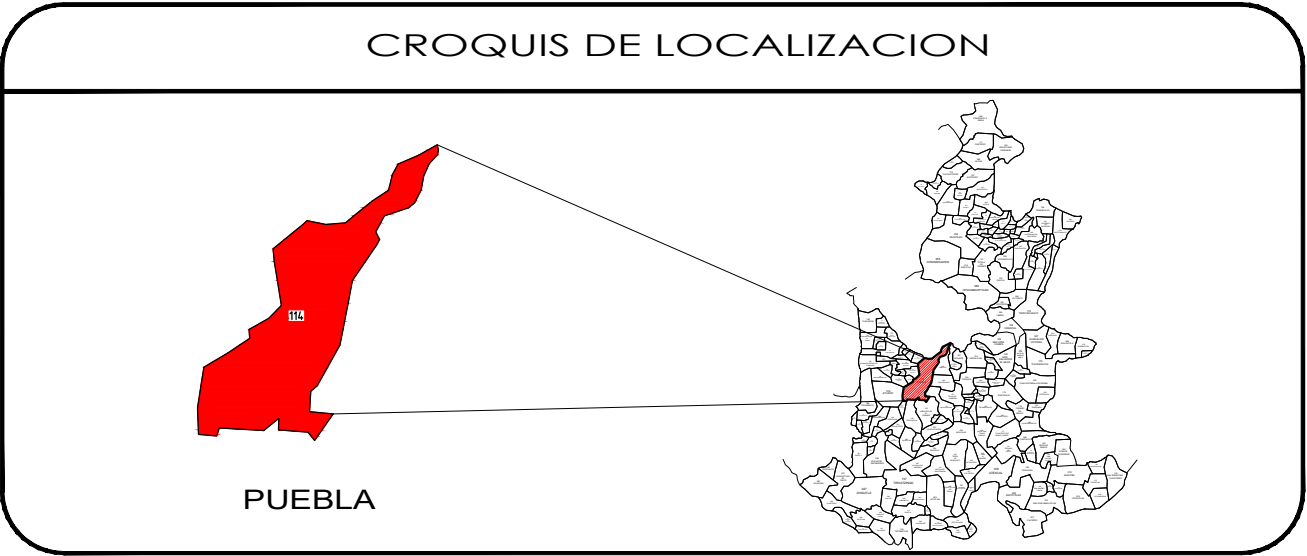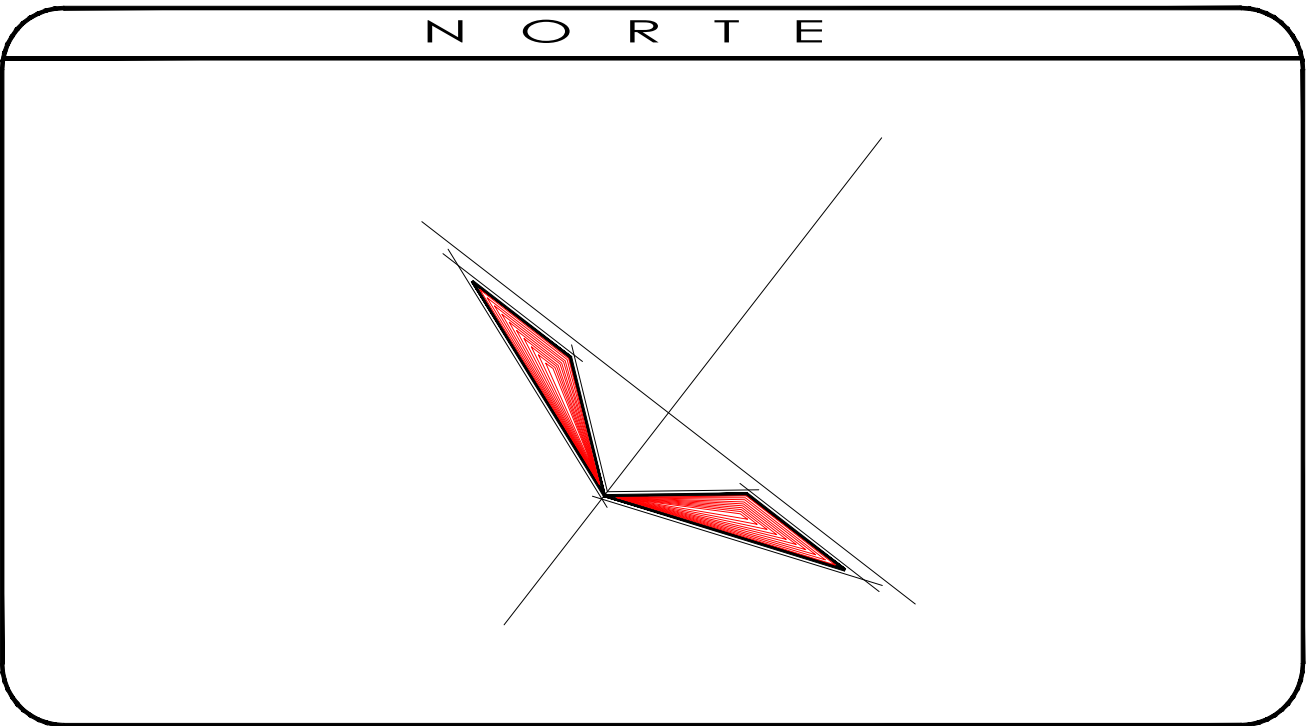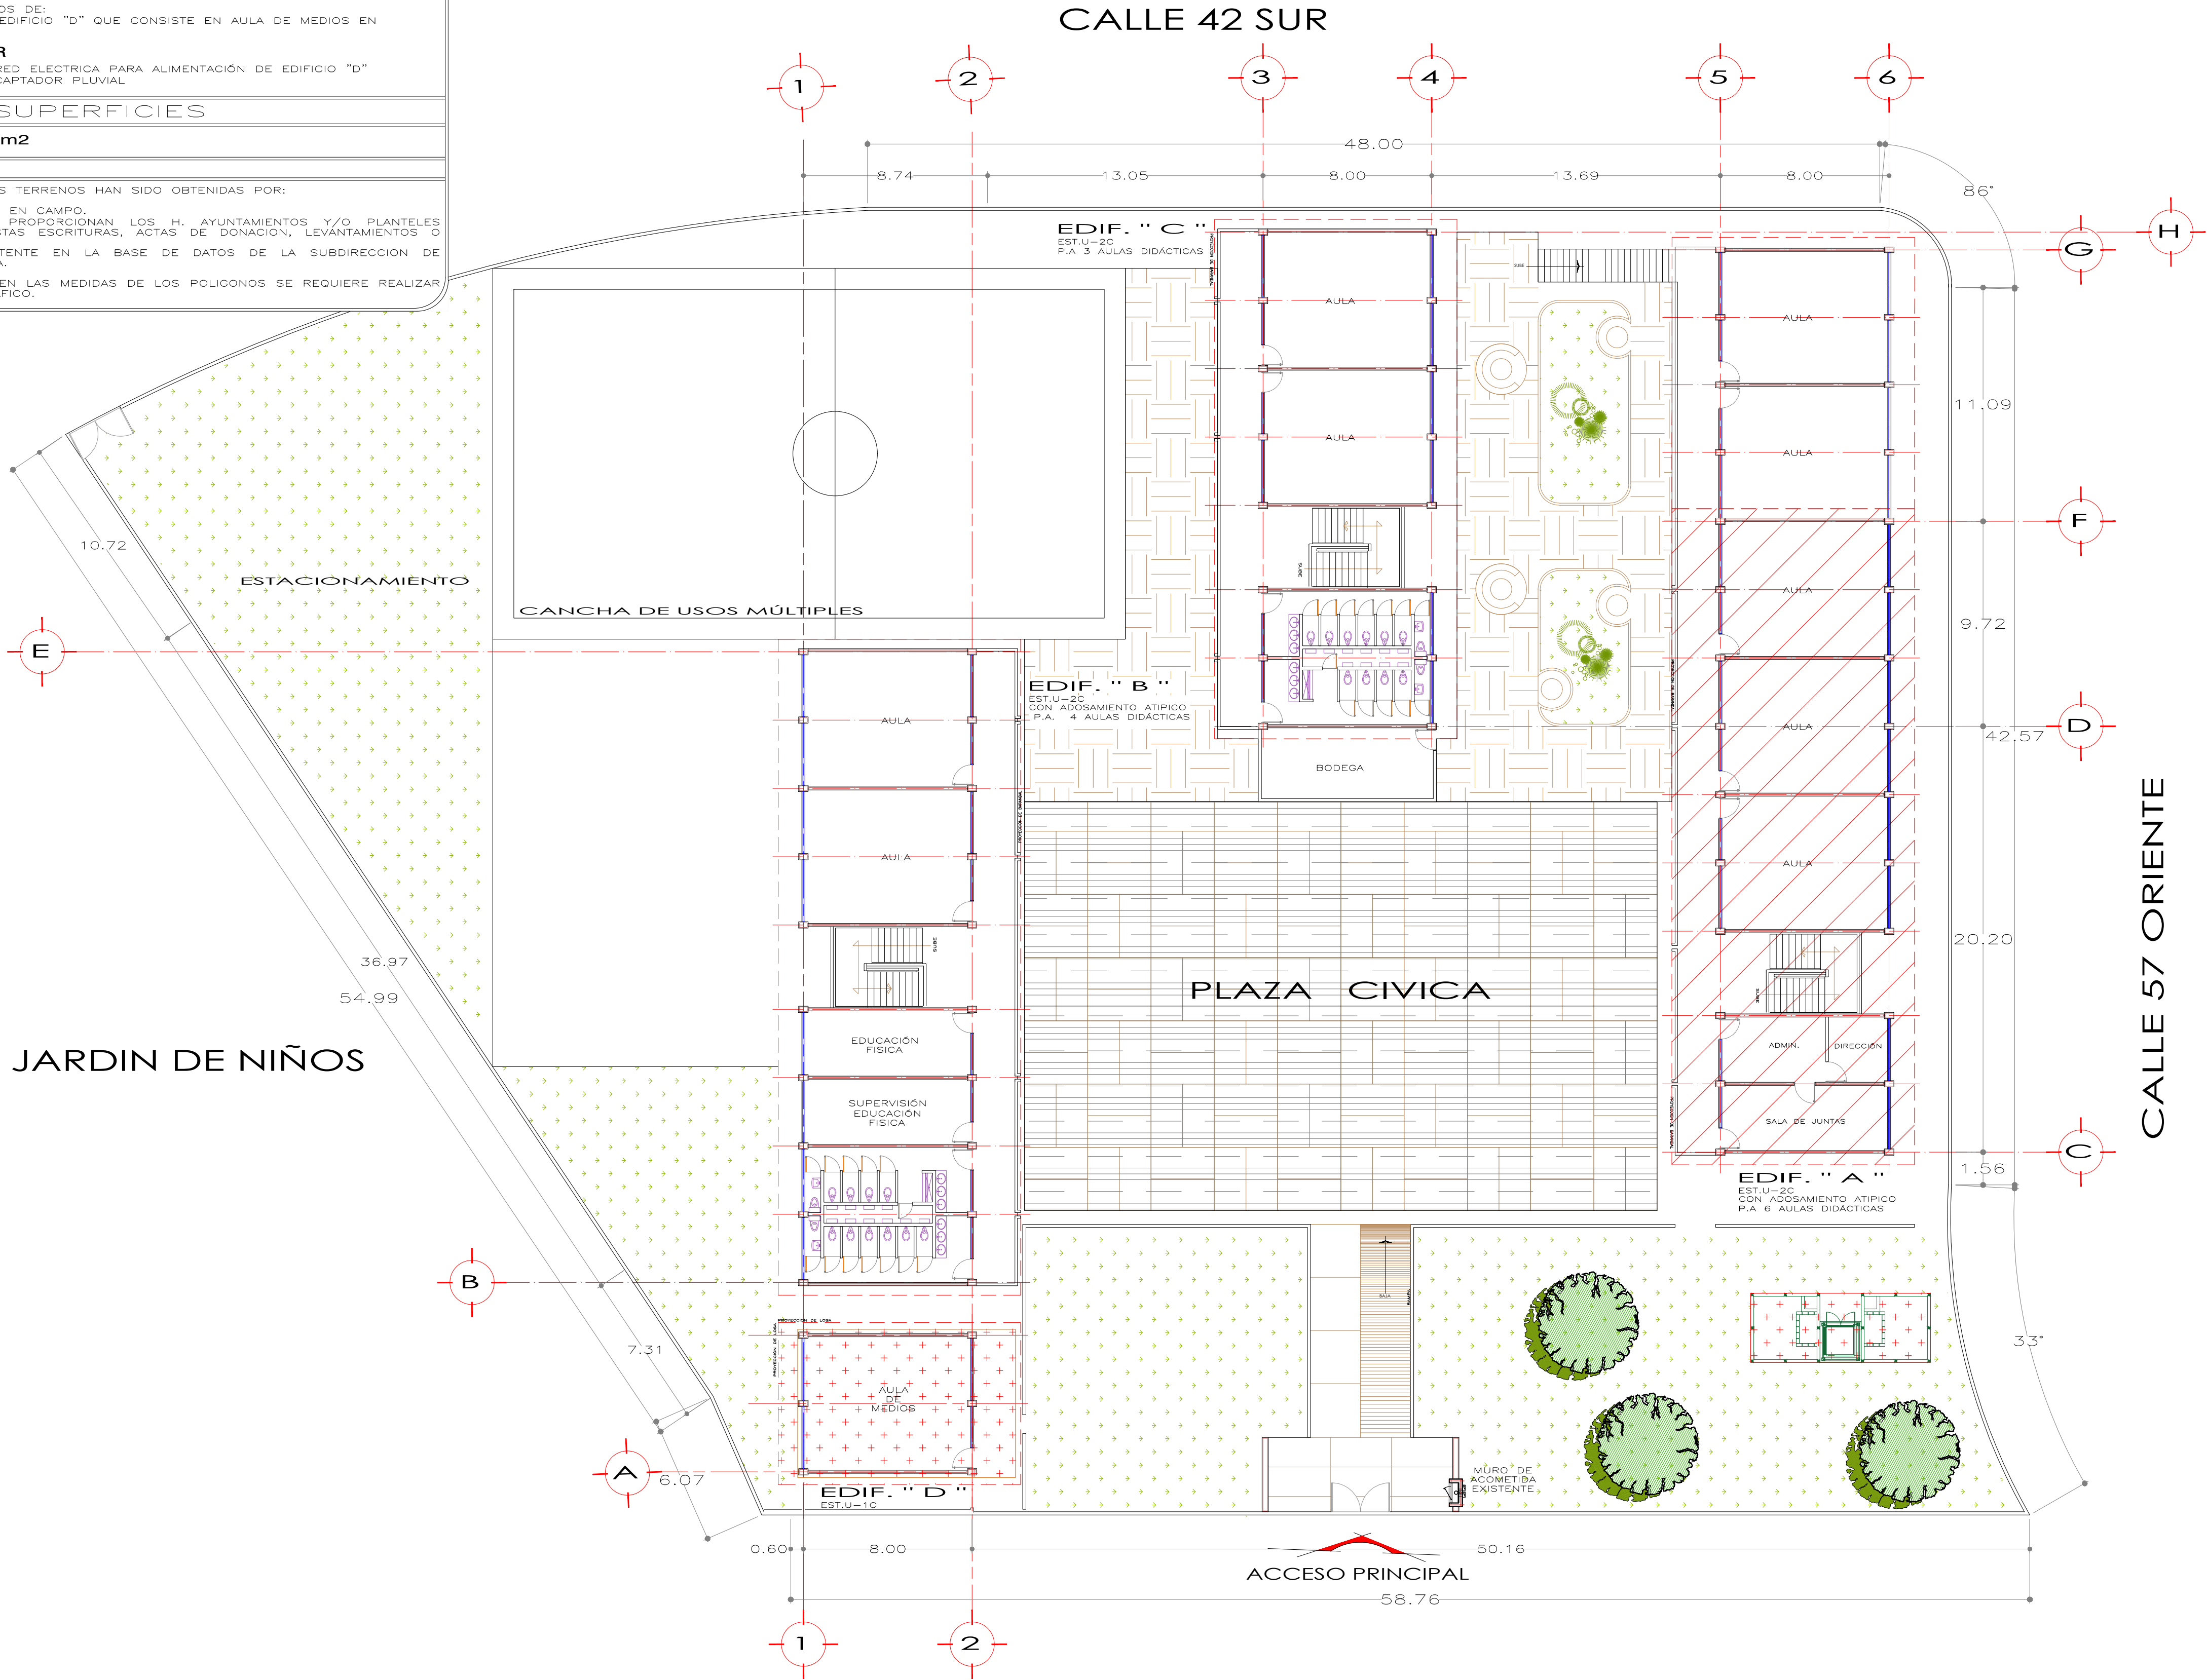

ETAPAS DE CONSTRUCCION		
ETAPA	A Ñ O	EDIFICIO
	EXISTENTE	"A,B,C"
+	2025	CONSTRUCCIÓN DE AULA DE MEDIOS
		CONSTRUCCIÓN DE OBRA EXTERIOR

NOTAS

◦ ANTES DE INICIAR LA OBRA, REALIZAR UN TRAZO DEL PROYECTO COMPLETO.

◦ REPORTAR CUALQUIER MODIFICACION A LA SUBDIRECCION DE PROYECTOS.

◦ LOS PLANOS DE CONJUNTO SE UTILIZARAN COMO REFERENCIA DE TRAZO PARA EL SEMBRADO DE EDIFICIOS, SI SE REQUIEREN VOLUMETRIAS, AMUEBLADO, INSTALACIONES ASI COMO TIPO DE SISMICIDAD, VERIFICAR PLANOS A DETALLE CORRESPONDIENTES.

◦ OBRAS DE REPARACION: EL PLANO DE CONJUNTO SE ELABORA CON LOS DATOS CONTENIDOS EN LA CEDULA DE VALIDACION.

◦ OBRAS CON EDIFICACION DE NUEVA CREACION O CONSOLIDACION: EL PLANO DE CONJUNTO SE ELABORA CON DATOS CONTENIDOS EN CEDULA DE VALIDACION, LEVANTAMIENTO DE TERRENO, DEMANDA EDUCATIVA PARA APLICAR EL MODELO CORRESPONDIENTE.

◦ SUPERVISOR QUE ELABORO LA CEDULA DE VALIDACION: _____ CON FECHA: _____ PARA ATENDER LOS DIFERENTES PRO-GRAMAS DE OBRA, POR TAL MOTIVO SOLO SE DIBUJA EL ESTADO ACTUAL DE LA INFRAESTRUC-TURA EDUCATIVA EXISTENTE EN LA VISITA PROGRAMADA EN EL CASO DE REPARACIONES Y EN EDIFICACION CONFORME AL MODELO EDUCATIVO, NORMA CAPCEE Y DEPENDIENDO DE LOS SIG-DATOS COMPLEMENTARIOS: 1.-NIVEL EDUCATIVO ANALIZADO 2.-DATOS ESTADISTICOS 3.-LEVAN-TAMIENTO O CROQUIS ADECUADO PARA DIGITALIZAR.

◦ RESPETAR SEMBRADO DE ARBOLES ASI COMO ELEMENTOS HISTORICOS

LA EJECUCIÓN DE LOS TRABAJOS SE APEGARÁ A LOS VOLUMENES PLASMADOS EN EL CATÁLOGO DE CONCEPTOS, EN VIRTUD DE QUE EN ALGUNOS CASOS EL PROYECTO ABARCA CANTIDADES MAYORES A LAS QUE SE VAN A REALIZAR, ASÍ MISMO Y DEBIDO A QUE SE UTILIZÁN PLANOS TIPO, LOS TRABAJOS A REALIZAR PUEDEN VARIAR, POR LO QUE DEBERÁN APEGARSE A LAS DESCRIPCIONES EN CASO DE MATERIALES, RESISTENCIAS O DEMÁS, INDICADAS EN LAS ESPECIFICACIONES DE CONSTRUCCIÓN GENERALES Y PARTICULARES, LA MEMORIA DESCRIPTIVA, ASÍ COMO EL CATÁLOGO DE CONCEPTOS.



PUEBLA
Gobierno del Estado
2024-2030

Infraestructura
Secretaría de Infraestructura

CAPCEE
Comité Asesor de Planeación para la Construcción de Espacios Educativos

MTRO. CARLOS OCHOA RODRIGUEZ
DIRECTOR GENERAL DEL CAPCEE

ESCUELA: PRIMARIA "PROFESORA PAULINA MARAVER CORTES" C.C.T. 21EPR0565N
LOCALIDAD: HERÓICA PUEBLA DE ZARAGOZA
MUNICIPIO: PUEBLA
PLANO: CONJUNTO ARQUITECTÓNICO

ING. ARQ. ALBERTO IGNACIO OROZCO PINTOS
DIRECTOR DE PROYECTOS Y COSTOS

ARQ. OLIVIA CRISTINA BOHÓRQUEZ CONTRERAS
JEFE DE PROYECTOS
FIRMA: _____

ING. J. MARIO CRUZ C.
JEFE DE INSTALACIONES
FIRMA: _____

ARQ. FERNANDO FLORES LUNA
JEFE DPTO. ING. ESTRUCTURAL
FIRMA: _____

DIBUJO
ARQ. KARLA CRUZ TELLEZ
REVISÓ
ING. DAVID ELADIO LÓPEZ HERNÁNDEZ
ARCHIVO ELECTRONICO
Validacion/proyecto/edules1
PROYECTOS
ESQ. DC
S/E
ESQ.60x90
ACOTACION
METROS

FECHA:
2025
PLANO ARQ.
No.
A-01

FIRMA: _____